


FY22 PayGo SCHOOL SIGNS MAINTENANCE

FID #: 30100 0200431 5XXXXXX 103739 E07880 9999

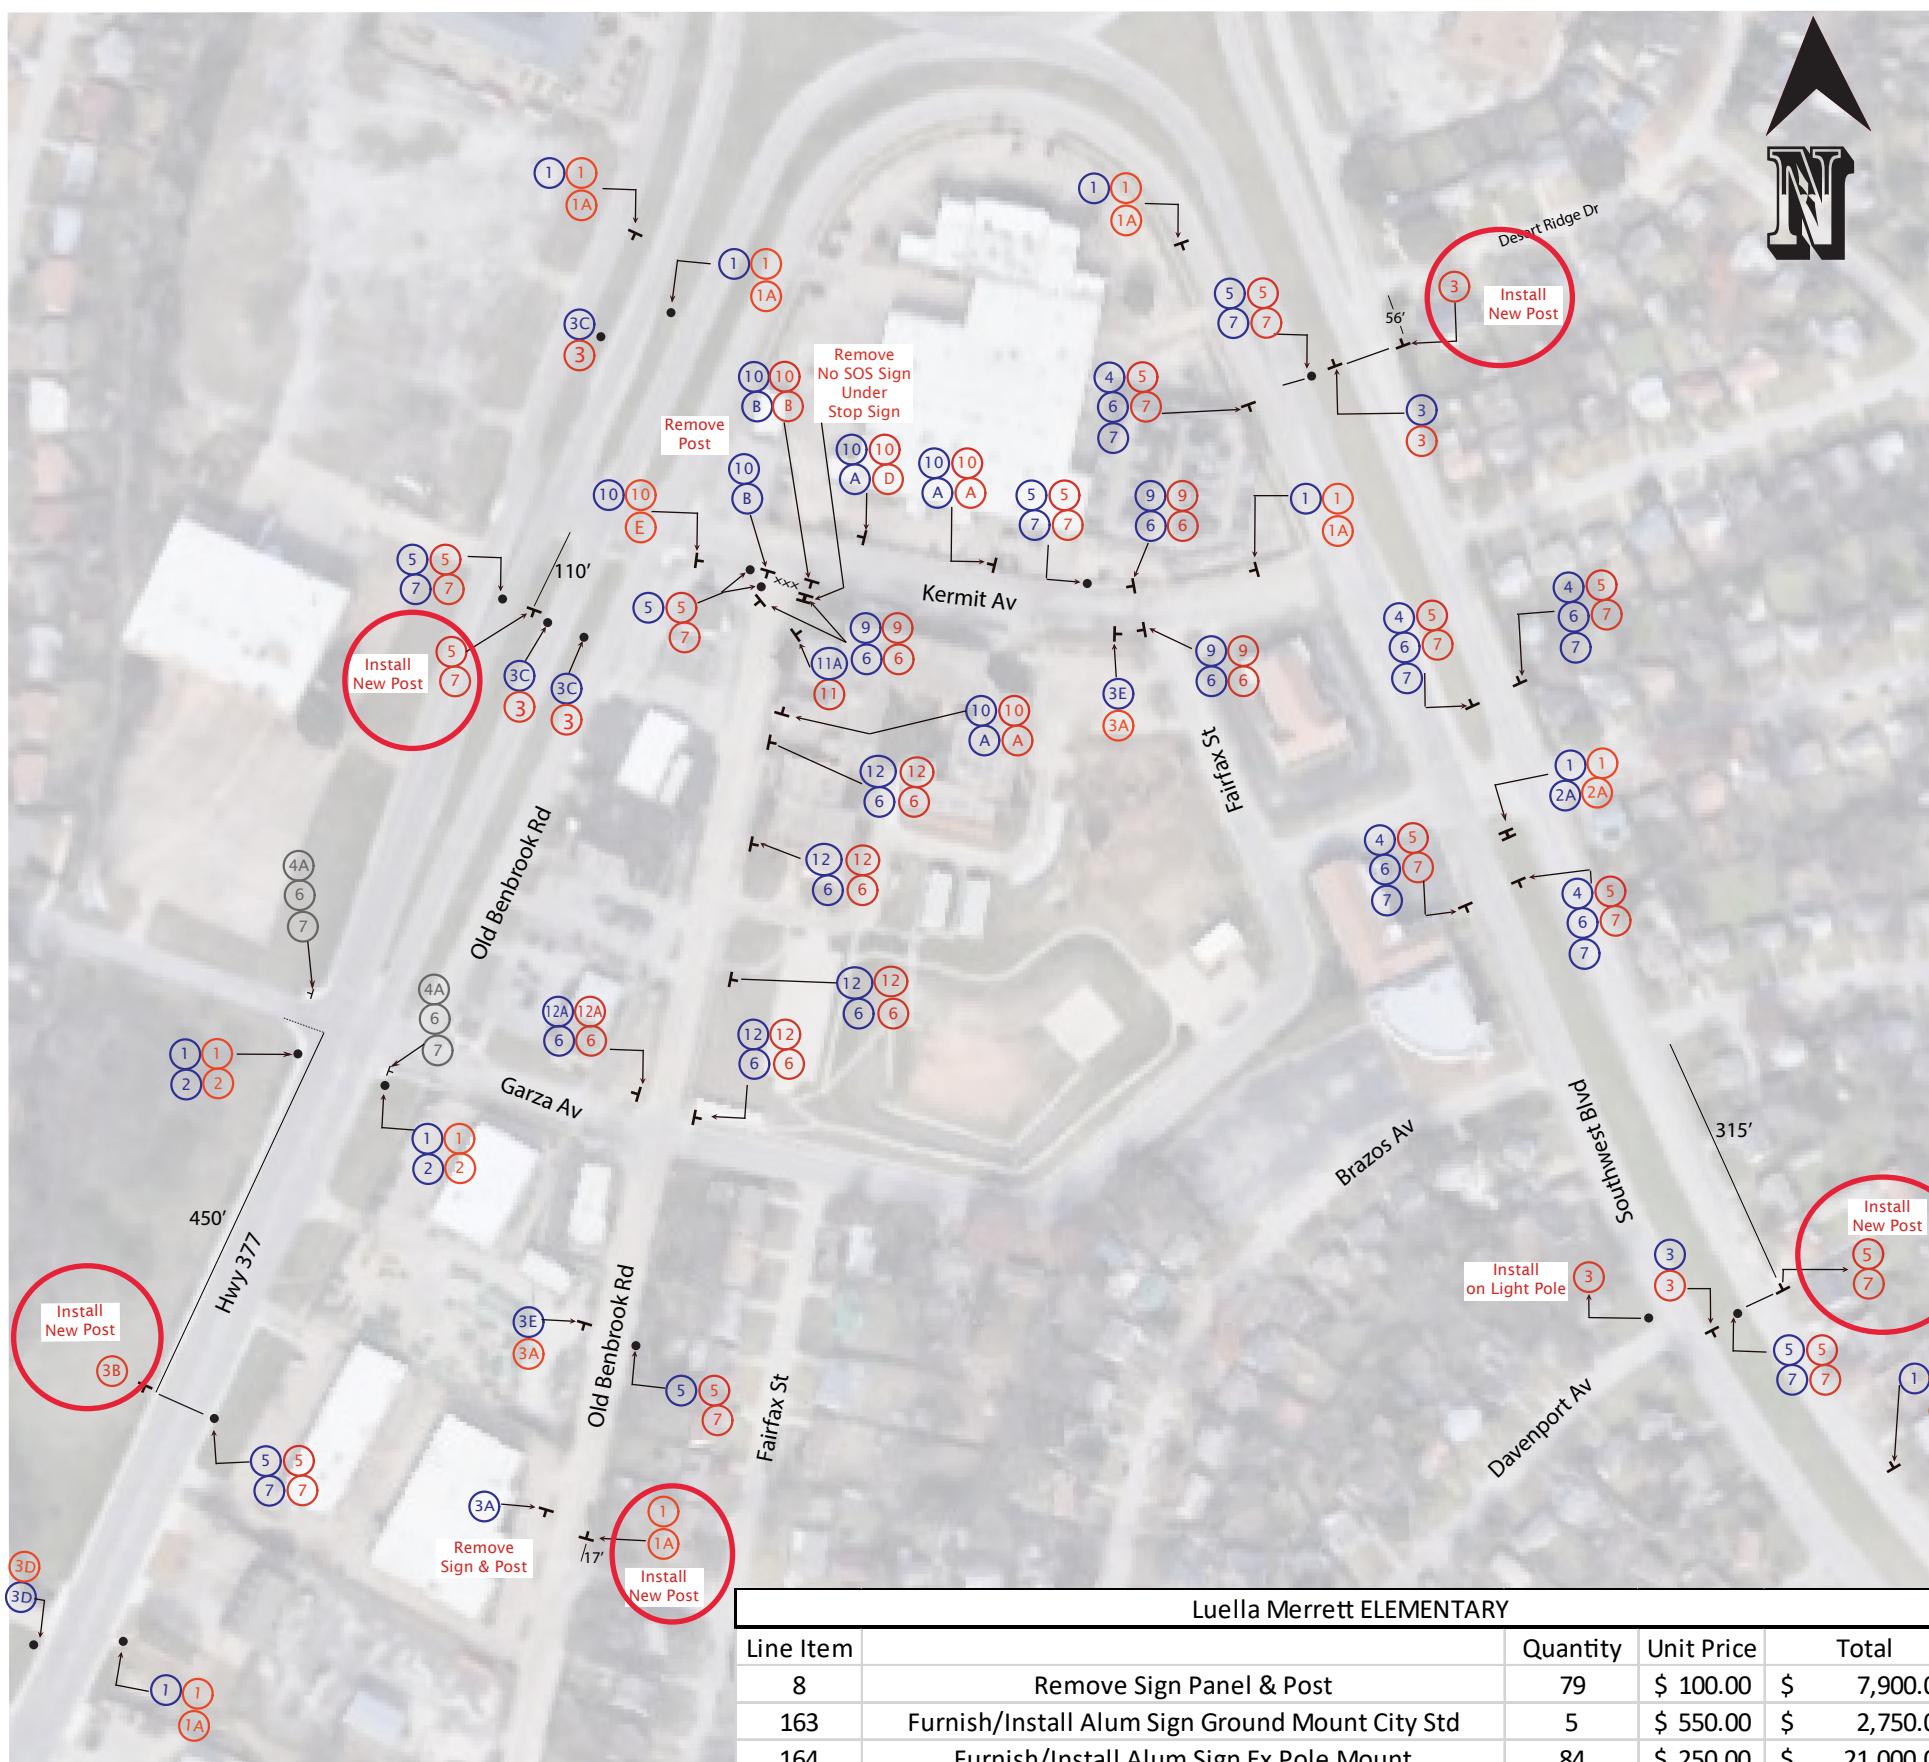

Luella Merrett ELEMENTARY				
Line Item		Quantity	Unit Price	Total
8	Remove Sign Panel & Post	79	\$ 100.00	\$ 7,900.00
163	Furnish/Install Alum Sign Ground Mount City Std	5	\$ 550.00	\$ 2,750.00
164	Furnish/Install Alum Sign Ex Pole Mount	84	\$ 250.00	\$ 21,000.00
				\$ 31,650.00

NO	1	2	3	3C	3A	3D	3E	4
	REMOVE SIGN	REMOVE SIGN	REMOVE SIGN	REMOVE SIGN	REMOVE SIGN	REMOVE SIGN	REMOVE SIGN	REMOVE SIGN
REMOVAL SIGN TYPE								
S1-1 36" Pentagon	W16-7P 2 2A	END SCHOOL ZONE SPEED LIMIT 35	S5-2a 24"x36"	R2-1-35 24"x30"	R2-1-35 24"x30"	SPEED LIMIT 30	SPEED LIMIT 45	END SCHOOL ZONE SCHOOL SPEED LIMIT 20
10	2	2	5	1	1	2	2	5

5	6	7	9	10	A	B	11B	12	12A
REMOVE SIGN	REMOVE SIGN	REMOVE SIGN	REMOVE SIGN	REMOVE SIGN	REMOVE SIGN	REMOVE SIGN	REMOVE SIGN	REMOVE SIGN	REMOVE SIGN
SCHOOL SPEED LIMIT 20 WHEN FLASHING	8:00-10:00 AM 3:00-5:00 PM SCHOOL DAYS	CELL PHONE USE PROHIBITED UP TO \$200 FINE	DO NOT ENTER	RAISED CROSSWALK	20 M.P.H.		NO STOPPING OR STANDING ANYTIME	ONE WAY	ONE WAY
S5-1 24"x48"	S4-1B 18"x24"	S7-1T 18"x24"					7AM-9AM 3PM-4PM SCHOOL DAY		
9	13	10	4	6	2	2	1	4	1

NO	1	1A	2	2A	3	3A	3C
WORK TYPE	FURNISH & INSTALL	FURNISH & INSTALL	FURNISH & INSTALL				
REMOVAL SIGN TYPE							
S1-1 36" Pentagon	AHEAD	W16-9P 36"x20"	W16-7P 30"x18"	W16-7P 30"x18"	END SCHOOL ZONE SPEED LIMIT 35	END SCHOOL ZONE SPEED LIMIT 30	SPEED LIMIT 35
11	6	2	2	2	2	2	3

NO	3D	5	6	7	9	10
FURNISH & INSTALL	FURNISH & INSTALL	FURNISH & INSTALL	FURNISH & INSTALL	FURNISH & INSTALL	FURNISH & INSTALL	FURNISH & INSTALL
REMOVAL SIGN TYPE						
SCHOOL SPEED LIMIT 45 WHEN FLASHING	7:00-9:00 AM 2:00-4:00 PM SCHOOL DAYS	CELL PHONE USE PROHIBITED UP TO \$200 FINE	DO NOT ENTER	RAISED CROSSWALK	20 M.P.H.	ONE WAY
S5-2a 30"x36"	S5-1 24"x48"	S4-1B 18"x24"	S7-1T 18"x24"	R5-1 30"x30"	W11-2 30"x30"	
1	14	9	14	4	6	

A	B	D	E	11	12	12A
FURNISH & INSTALL	FURNISH & INSTALL	FURNISH & INSTALL				
20 M.P.H.	RAISED CROSSWALK	24"x 12"	24"x 12"	NO STOPPING OR STANDING ANYTIME	CELL PHONE USE PROHIBITED UP TO \$200 FINE	ONE WAY
18"x 18"	36"x 9"	24"x 12"	24"x 12"	7AM-9AM 3PM-4PM SCHOOL DAY	7AM-9AM 3PM-4PM SCHOOL DAY	ONE WAY

SCALE
0 100 200

PROJECT ENG: M. CONLIN
PHONE: 817-392-8779
DRAWN BY: S. FLORES
REVIEWED BY: M. CONLIN
COMPLETE DATE: MARCH 1, 2022

NOTICE
VERIFY LOCATION OF ALL EXISTING
UNDERGROUND UTILITIES

SCOPE: School Maintenance



PROPOSED LAYOUT

Luella Merrett Elementary
7325 Kermit Av